




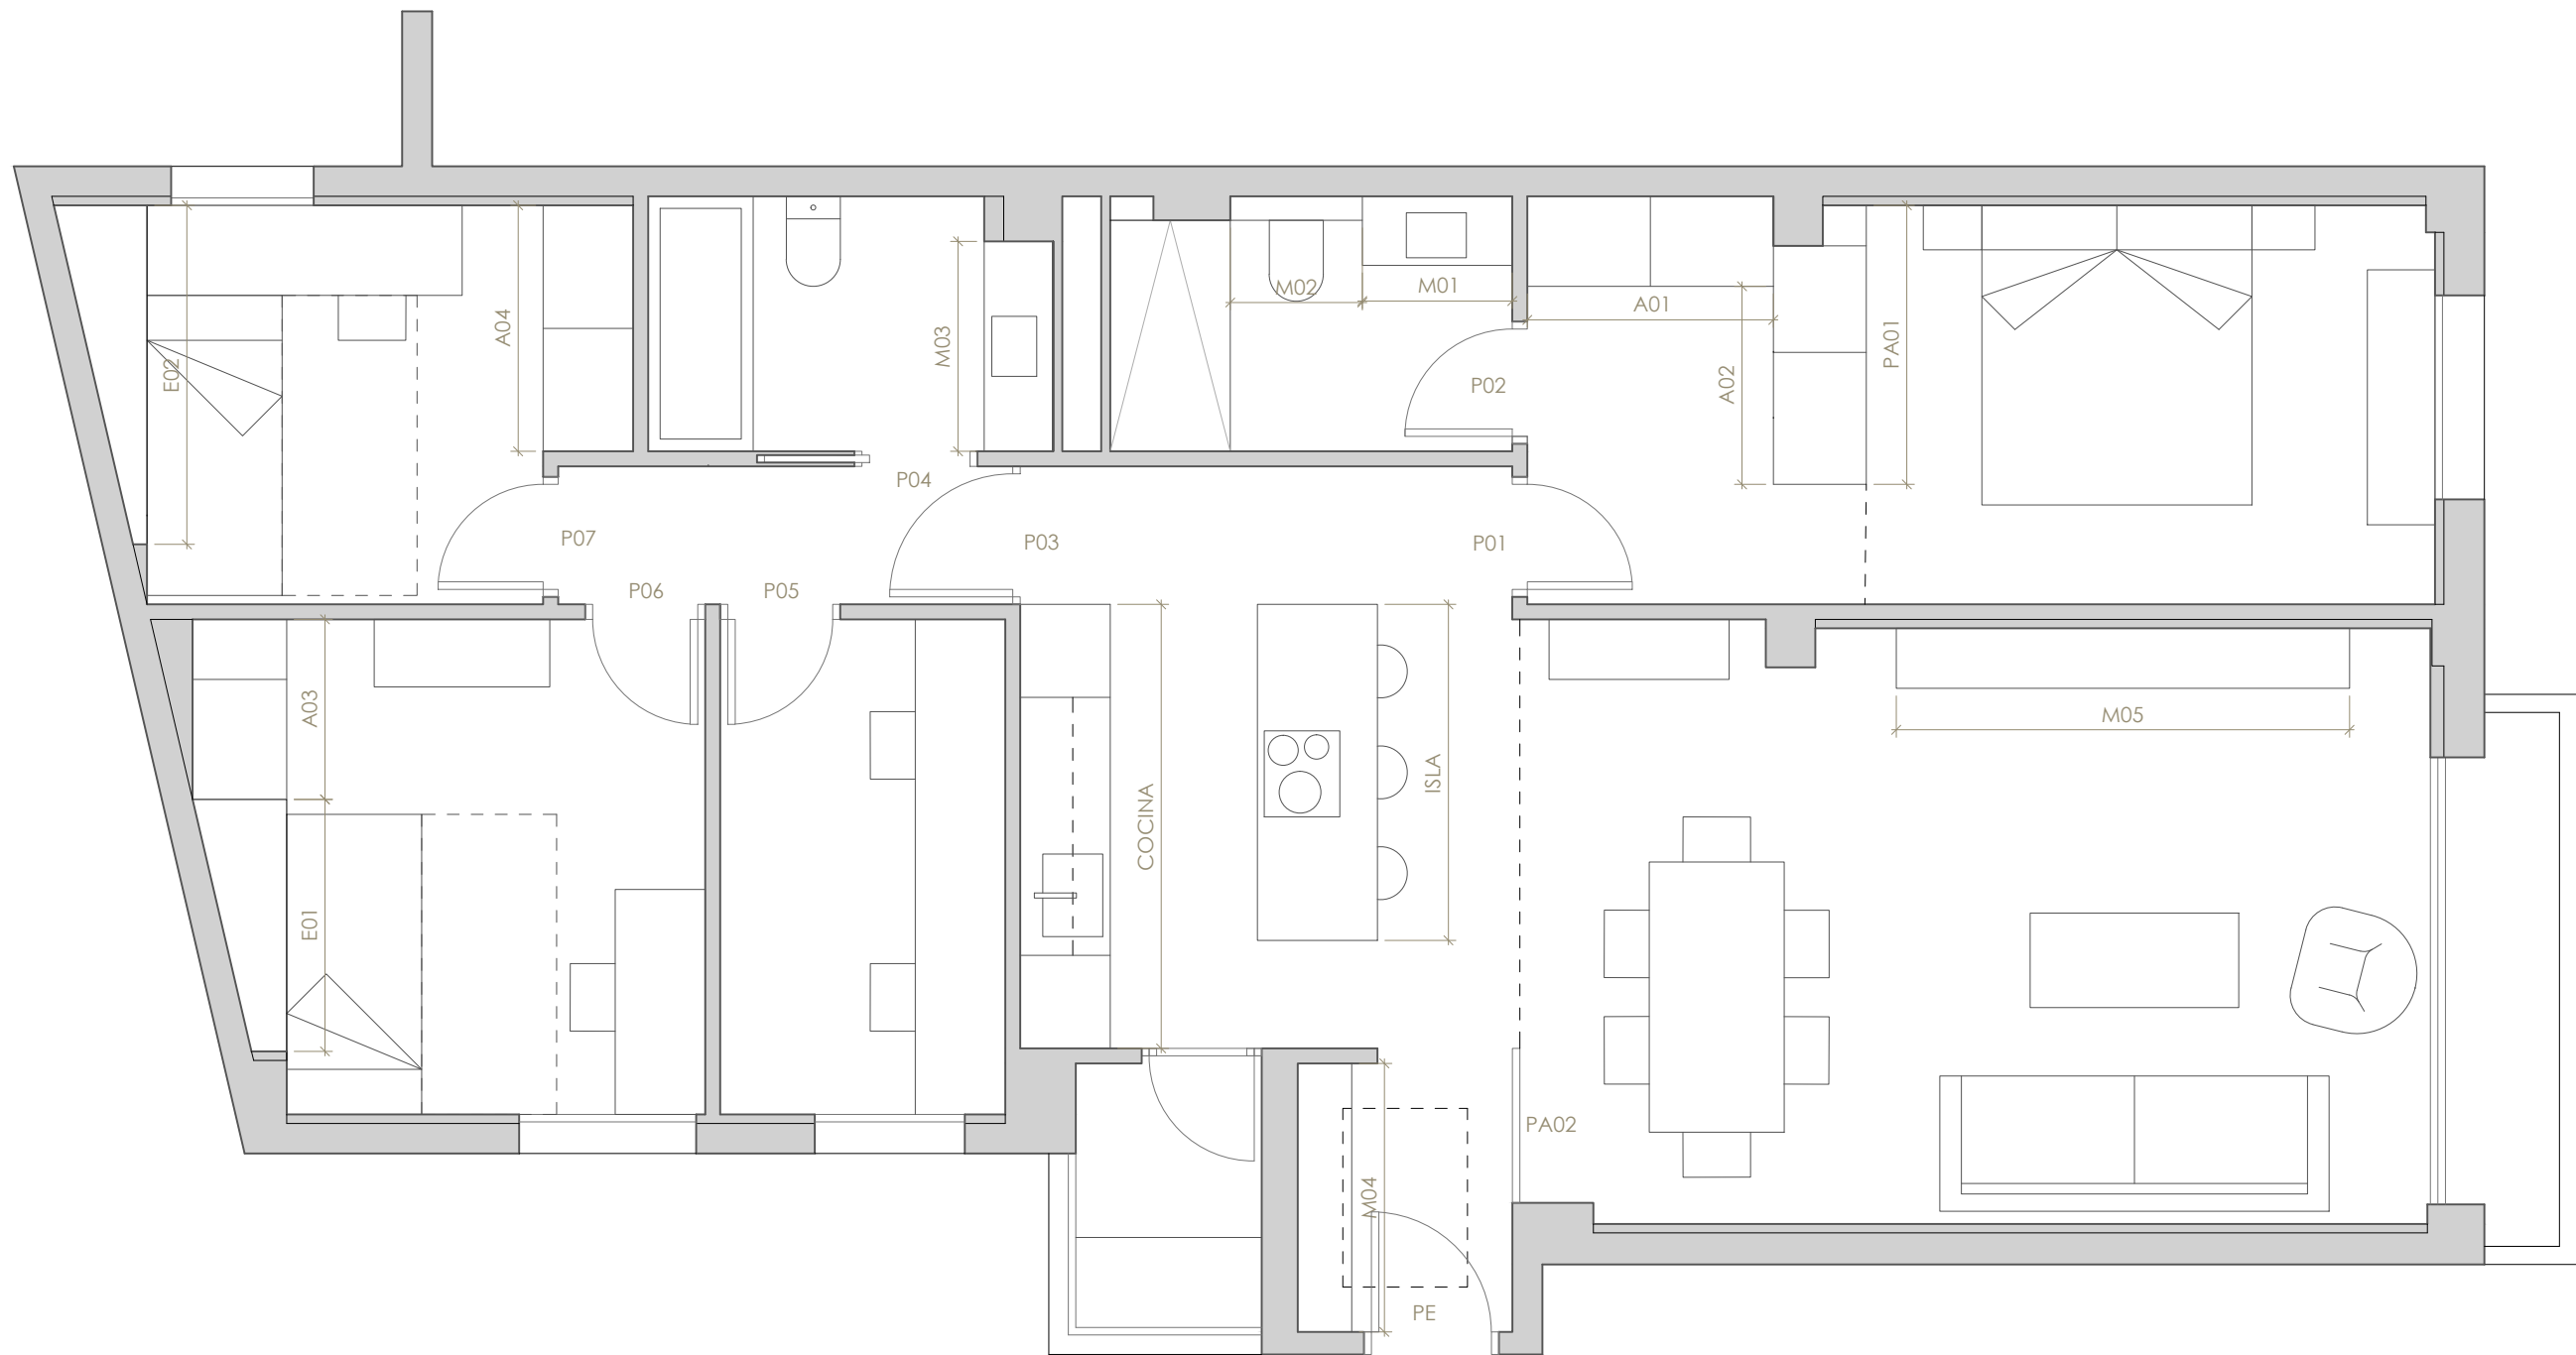


COCINA

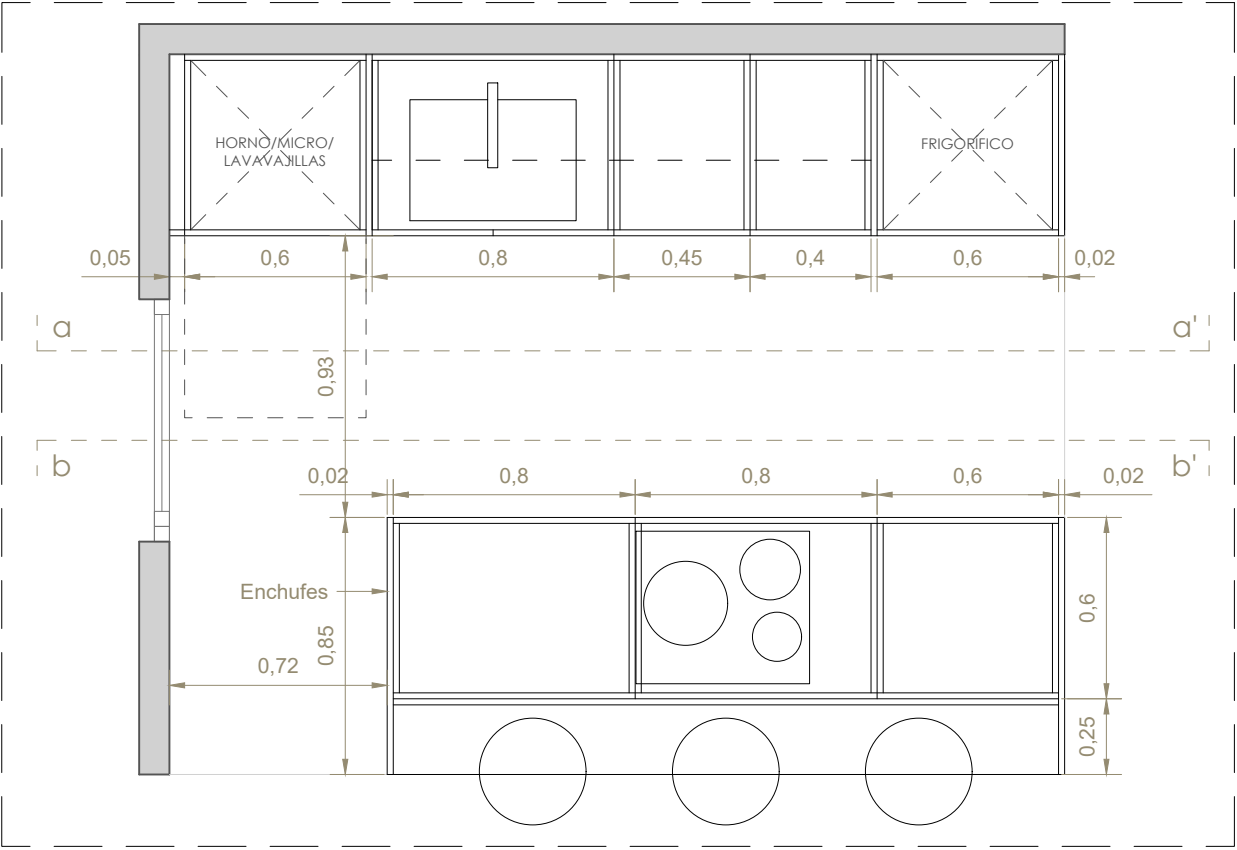

MOBILIARIO COCINA


- Exterior en melamina imitación roble e interior en melamina gris oscuro.
- Apertura muebles con uñero integrado, columnas con tirador metálico a elegir.
- Isla en melamina gris grafito satinada, lo más parecido a la encimera, interior en melamina gris oscuro.
- Perfil para tira led con difusor integrado en armarios altos.
- Laterales y frontal isla en encimera de porcelánico.

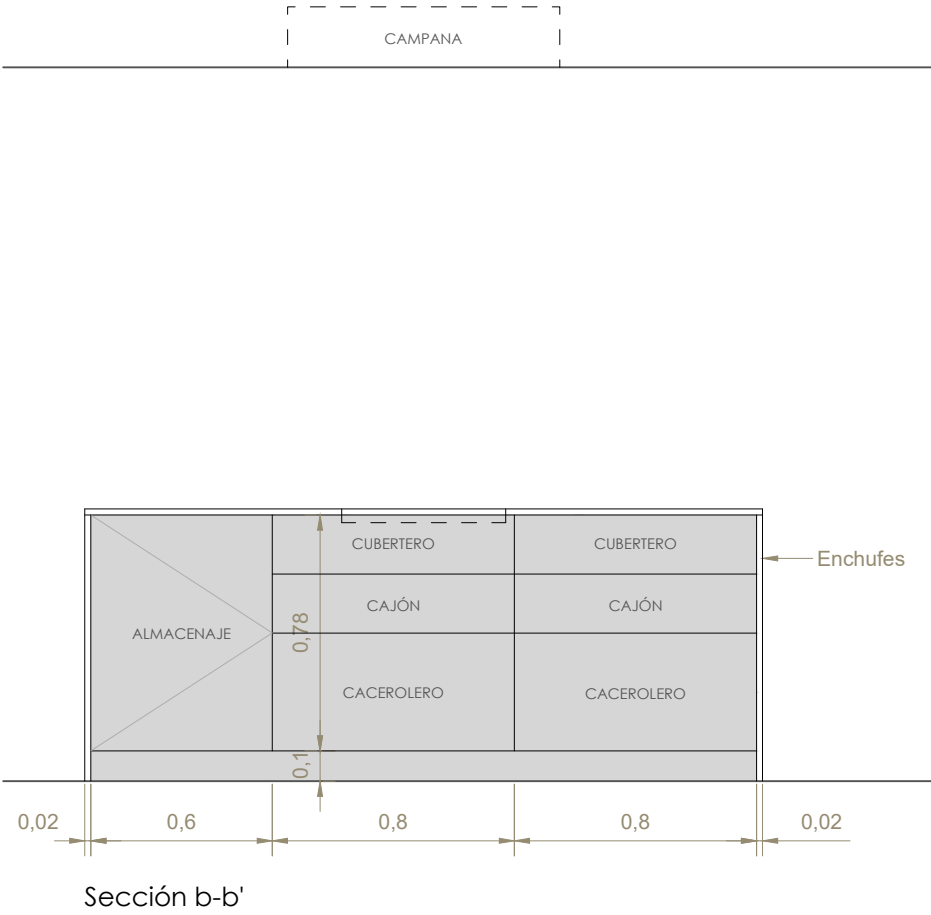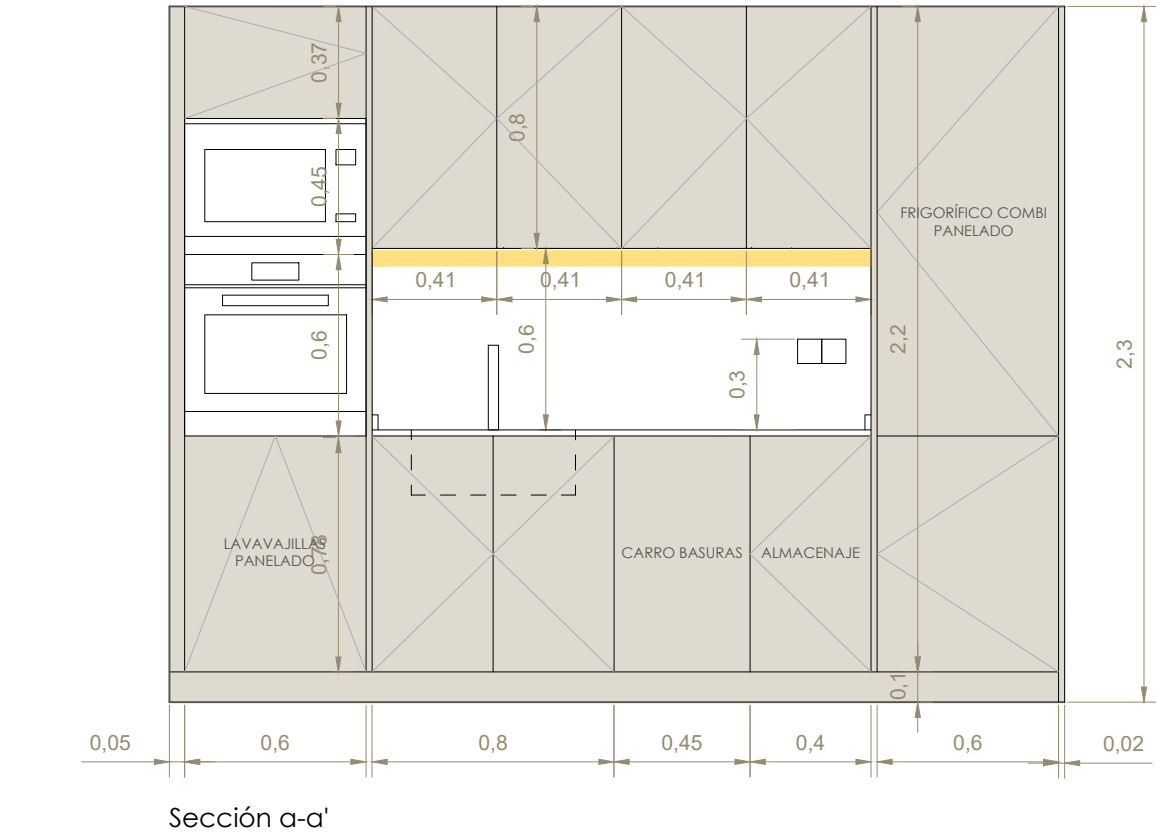

ARMARIOS


A01 ARMARIO DORMITORIO PRINCIPAL

- Exterior melamina imitación roble e interior en melamina textil.
- Apertura armarios tirador metálico a definir.

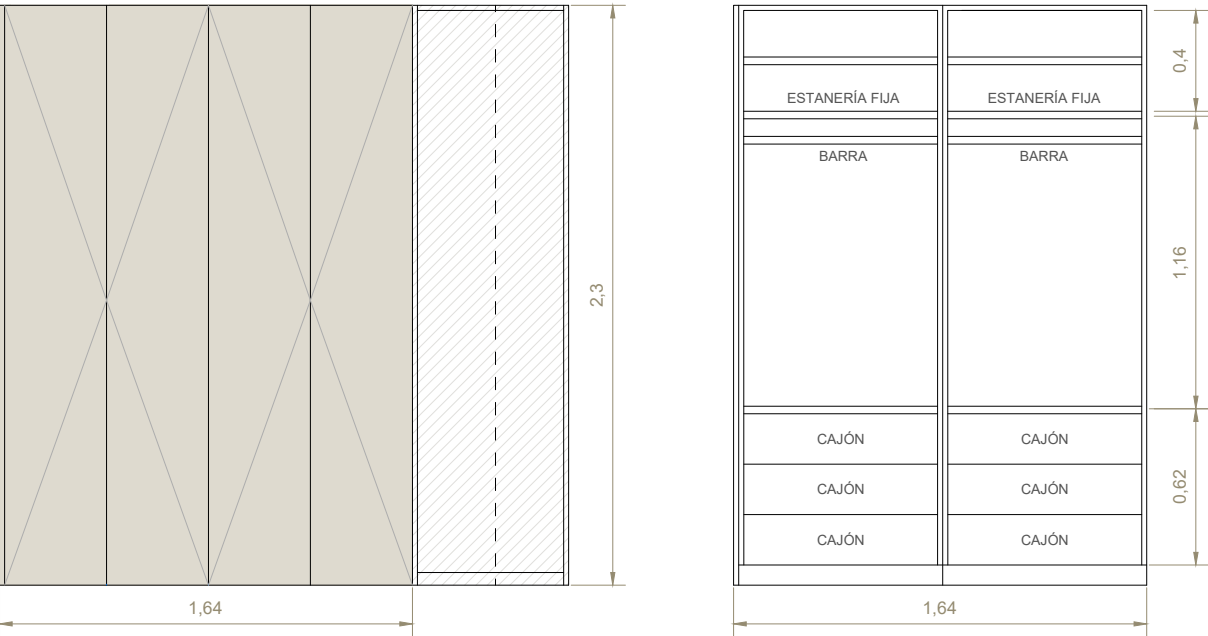


A02 ARMARIO DORMITORIO PRINCIPAL

- Exterior melamina imitación roble e interior en melamina textil.
- Apertura armarios tirador metálico a definir.

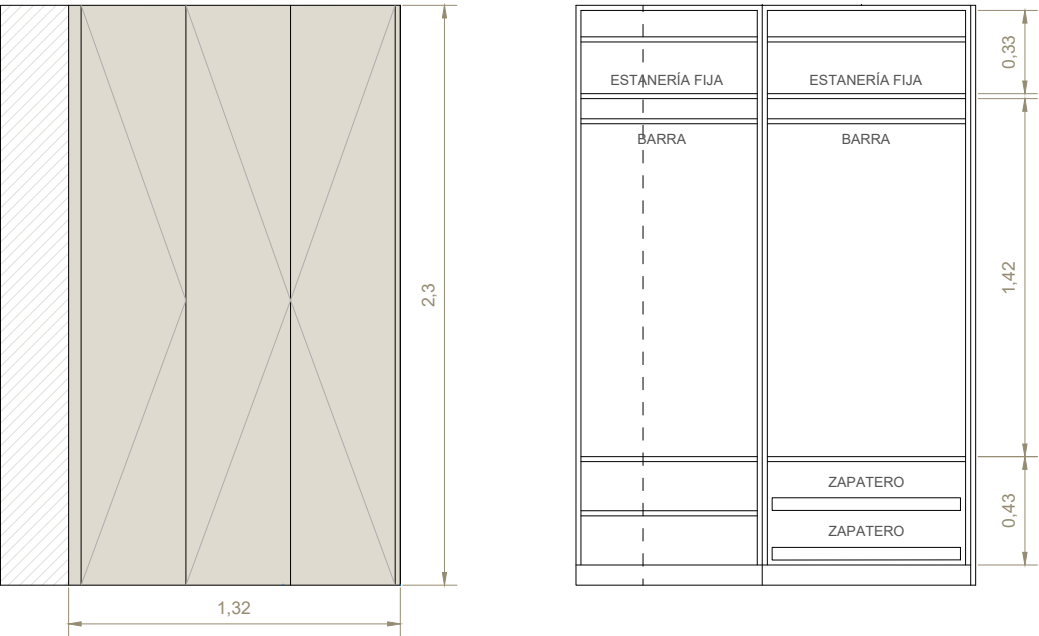


PANELADOS

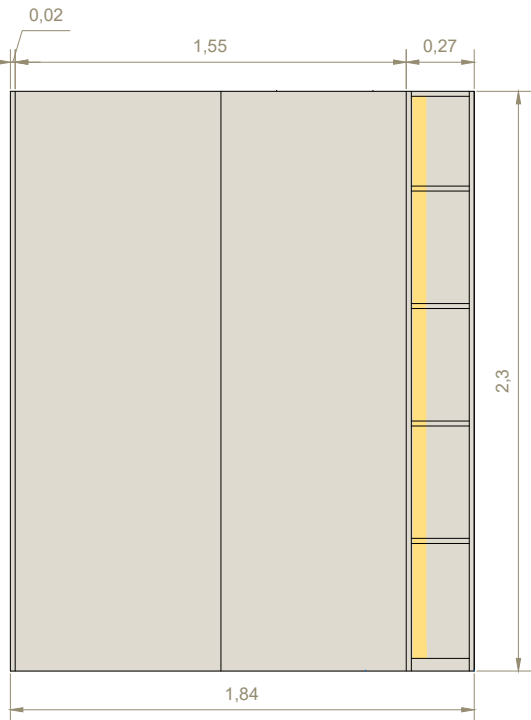

PA01 PANELADO Y ESTANERÍA DORMITORIO PRINCIPAL

- Panleado y estatería en melamina imitación roble.
- Baldas fijas.
- Tira led integrada.

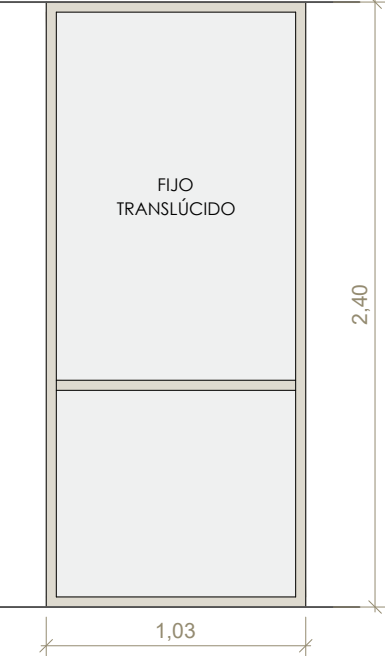

PA02 SEPARADOR AMBIENTE RECIBIDOR



- Separador de ambiente de recibidor fijo.
- Vidrio acabado al ácido.
- Marco de perfil de madera de 4 cm de espesor.



ARMARIOS



A03 ARMARIO DORMITORIO 2

- Exterior melamina imitación roble e interior en melamina textil.
- Apertura armarios tirador metálico a definir.

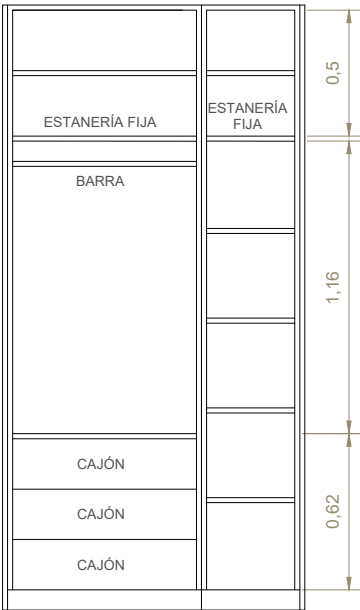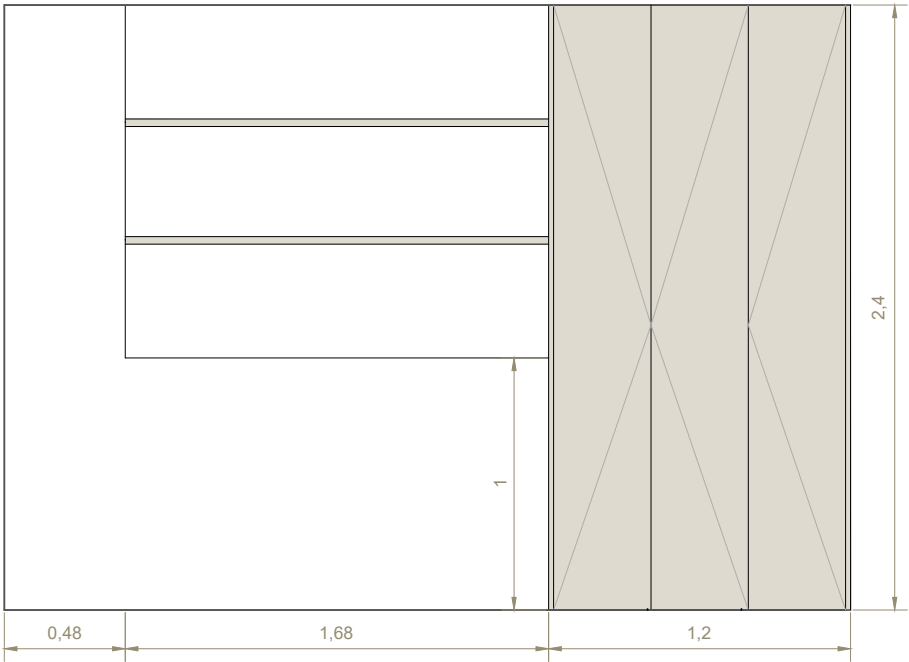

A04 ARMARIO DORMITORIO 3


- Exterior melamina imitación roble e interior en melamina textil.
- Apertura armarios tirador metálico a definir.

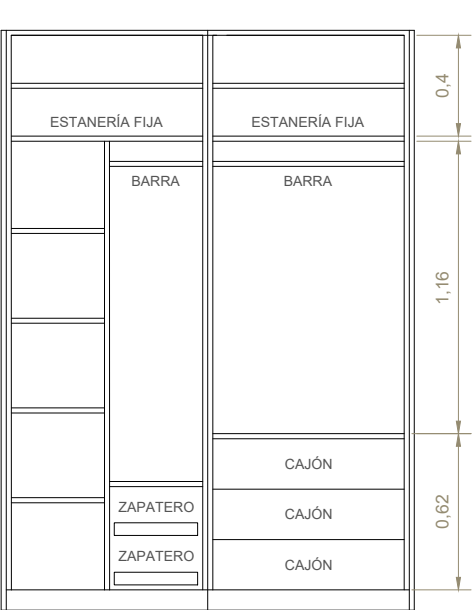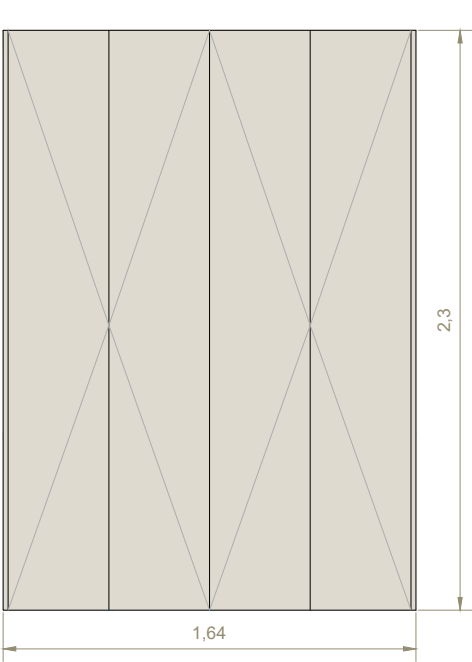

ESTANTERÍAS


E01 ESTANTERÍA DORMITORIO 2

- Estanterías fija de 2 baldas de 4 cm de espesor.
- Exterior melamina imitación roble.

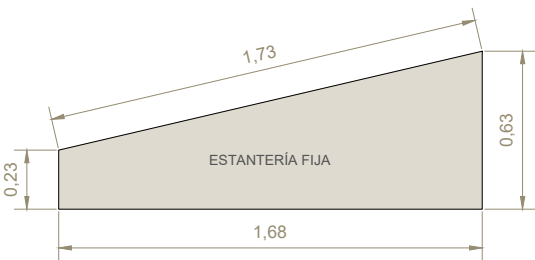

E02 ESTANTERÍA DORMITORIO 3


- Estantería fija de 2 baldas de 4 cm de espesor.
- Exterior melamina imitación roble.

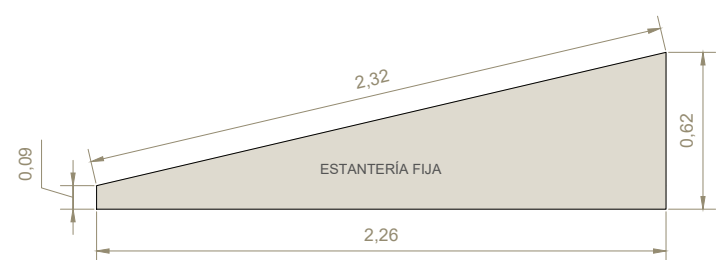

MUEBLES


M01 MUEBLE LAVABO BAÑO 1

- Mueble de lavabo suspendido
- Exterior melamina imitación roble e interior en melamina textil.
- Apertura armarios uñero integrado.
- Led empotrado y encimera resina.

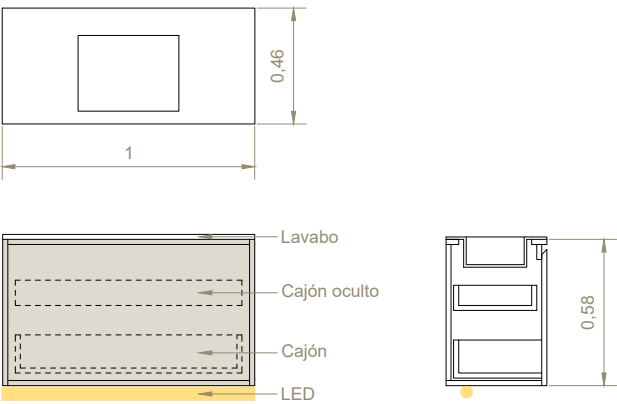


M02 MUEBLE BAÑO

- Mueble de baño empotrado
- Exterior lacado blanco e interior en melamina textil.
- Apertura armarios uñero integrado.

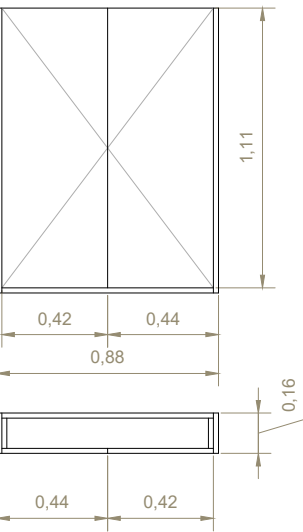


M01 MUEBLE LAVABO BAÑO 2

- Mueble de lavabo suspendido
- Exterior melamina imitación roble e interior en melamina textil.
- Apertura armarios uñero integrado.
- Led empotrado y encimera resina.

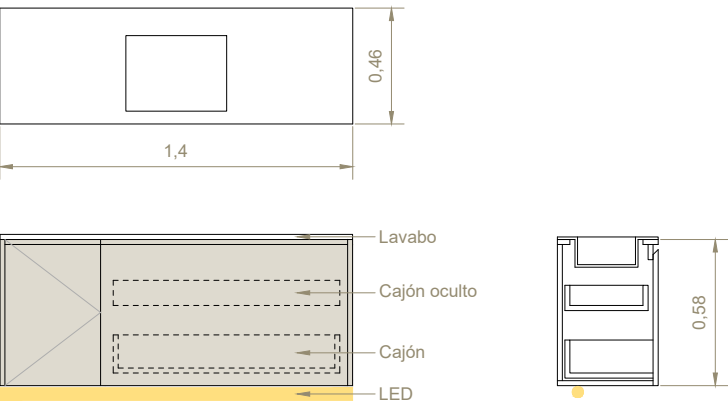


M04 MUEBLE ZAPATERO

- Mueble zapatero suspendido
- Exterior melamina imitación madera e interior en melamina textil.
- Apertura armarios uñero integrado.
- Led empotrado

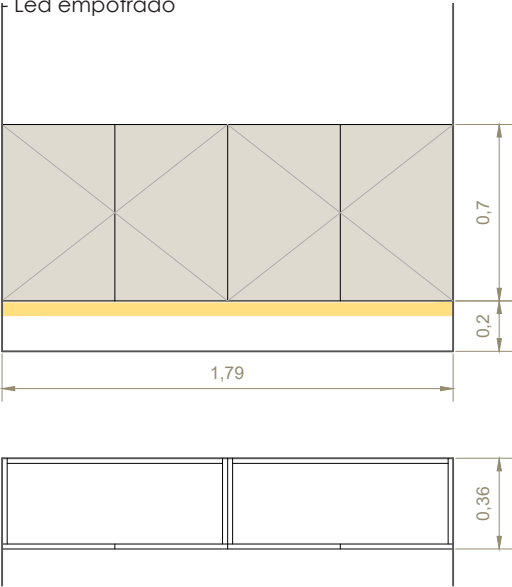


M05 MUEBLE TV

- Mueble de TV sin suspender.
- Exterior melamina imitación madera e interior en melamina textil.
- Apertura armarios uñero integrado.

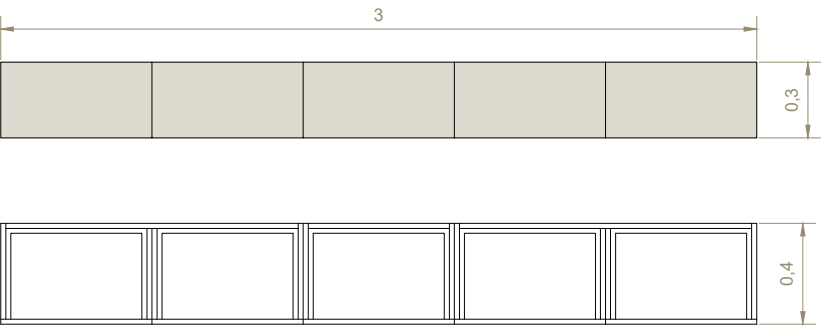

PUERTAS

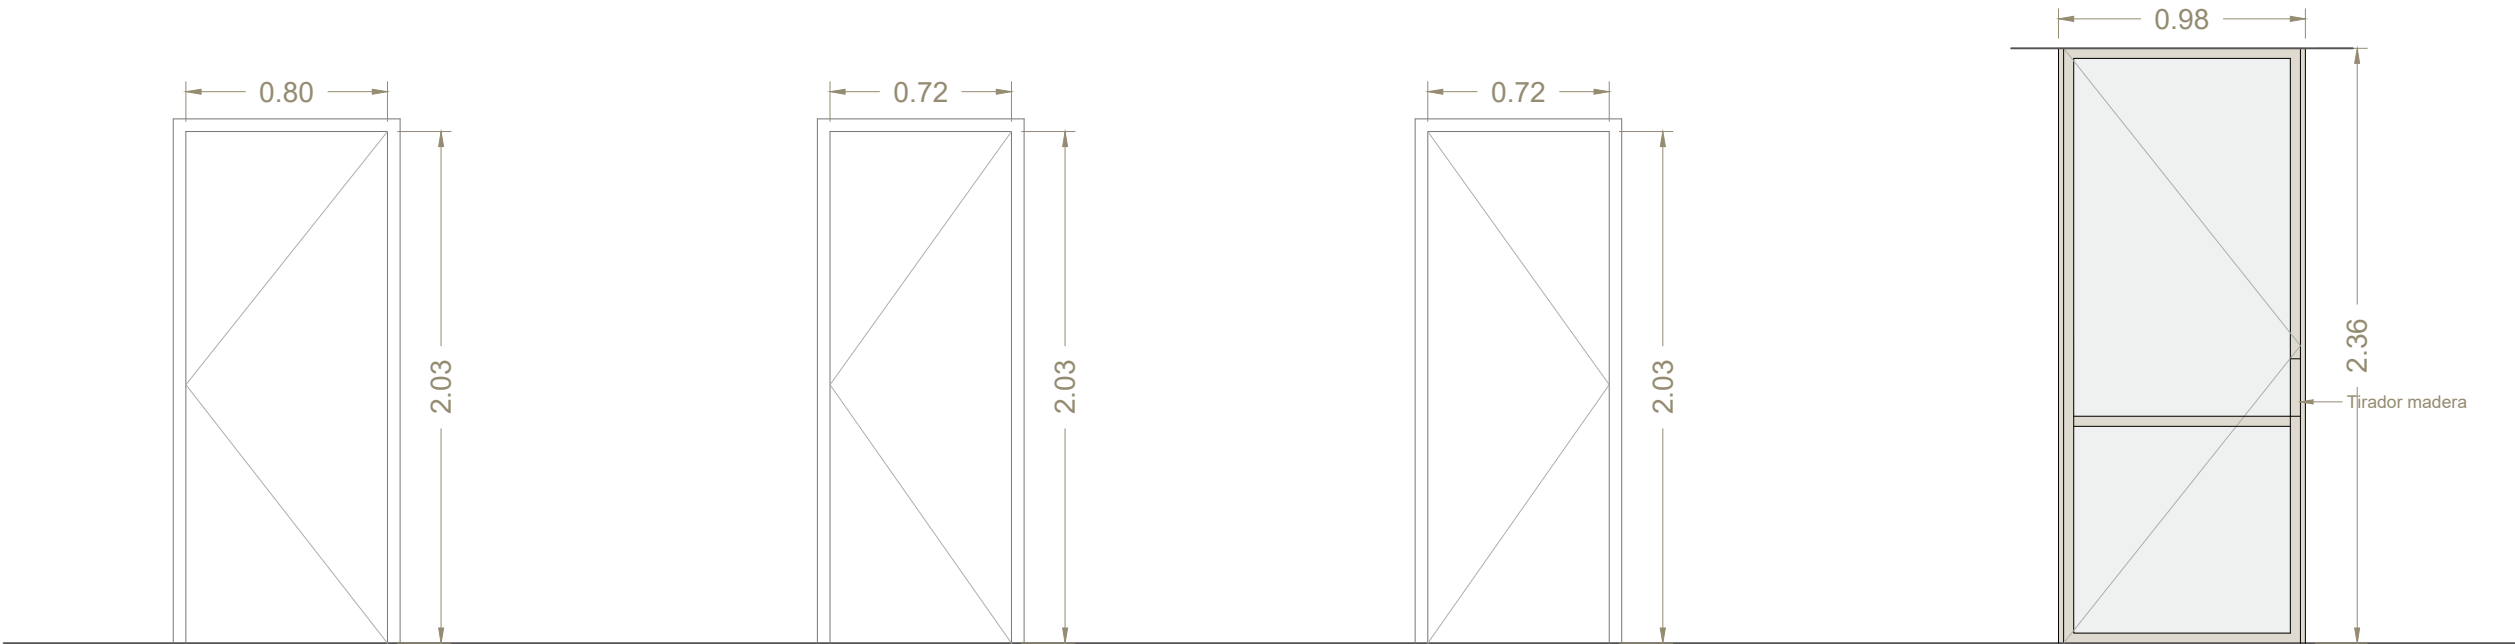


PE
Panelado en lacado blanco de puerta existente
Cambio de herrajes y manivela

P01
Puerta abatible
Acabado lacado blanco
Con condena
Herrajes y manivela metálicos blancos a definir

P02
Puerta abatible
Acabado lacado blanco
Con condena
Herrajes y manivela metálicos blancos a definir

P03
Puerta abatible de suelo a techo
Madera natural
Tirador a medida madera
Cristal tranlúcido

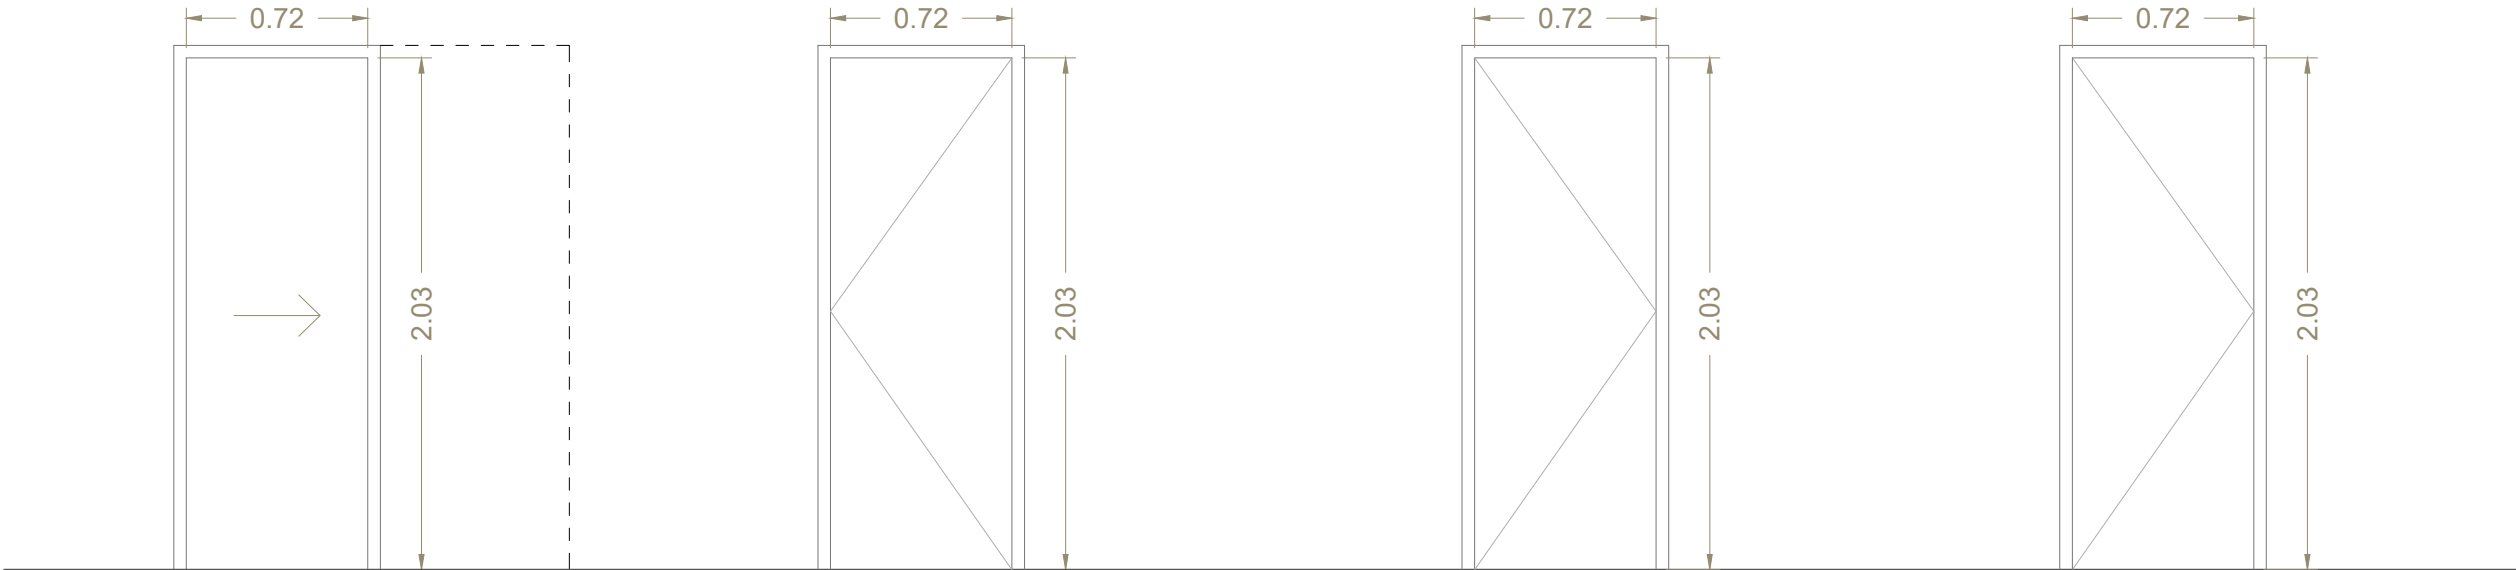

P04
Puerta corerdera
Acabado lacado blanco
Con condena
Uñero metálico blanco a definir

P05
Puerta abatible
Acabado lacado blanco
Con condena
Herrajes y manivela metálicos blancos a definir

P06
Puerta abatible
Acabado lacado blanco
Con condena
Herrajes y manivela metálicos blancos a definir

P07
Puerta abatible
Acabado lacado blanco
Con condena
Herrajes y manivela metálicos blancos a definir

