


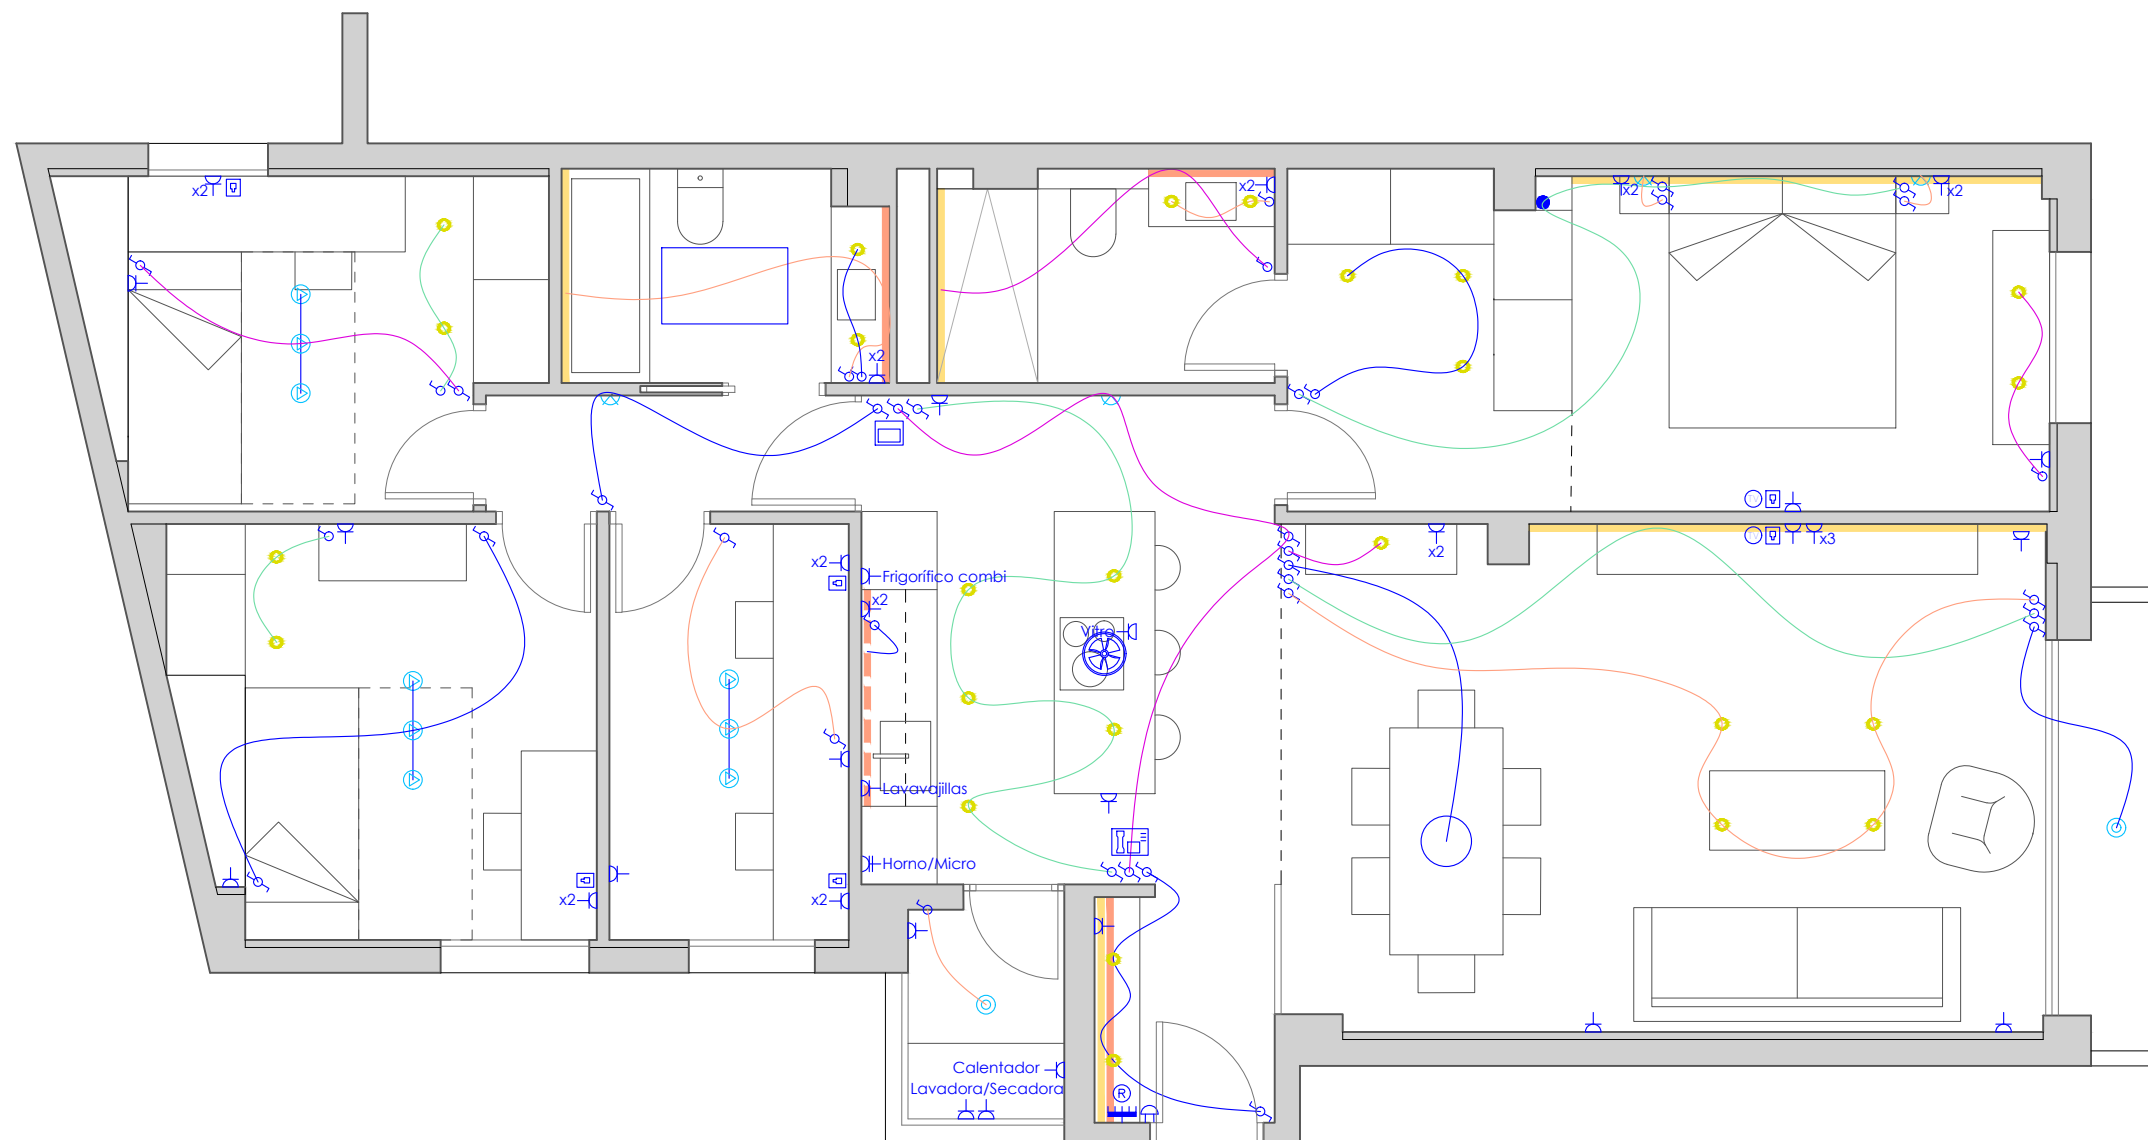

- Cuadro eléctrico general
- Toma corriente 16A
- Toma corriente 25A
- Interruptor
- Interruptor conmutado
- Toma TV
- Router
- Timbre
- Telefonillo
- Termostato ACC
- Campana extractora
- Luminaria empotrada techo
- Riel focos superficie techo
- Foco superficie techo
- Aplique pared
- Tira LED oscuro pladur 3000K 20W
- Tira LED encastrada en mueble 3000K 20W
- Tira LED encastrada mueble 4000K 20W

La altura general de los mecanismos será h=110 cm hacia abajo.

